


Schlossgasse 9, 4103 Bottmingen

DEMO - synthetisch, keine echten Objektdaten


UNTERGESCHOSS

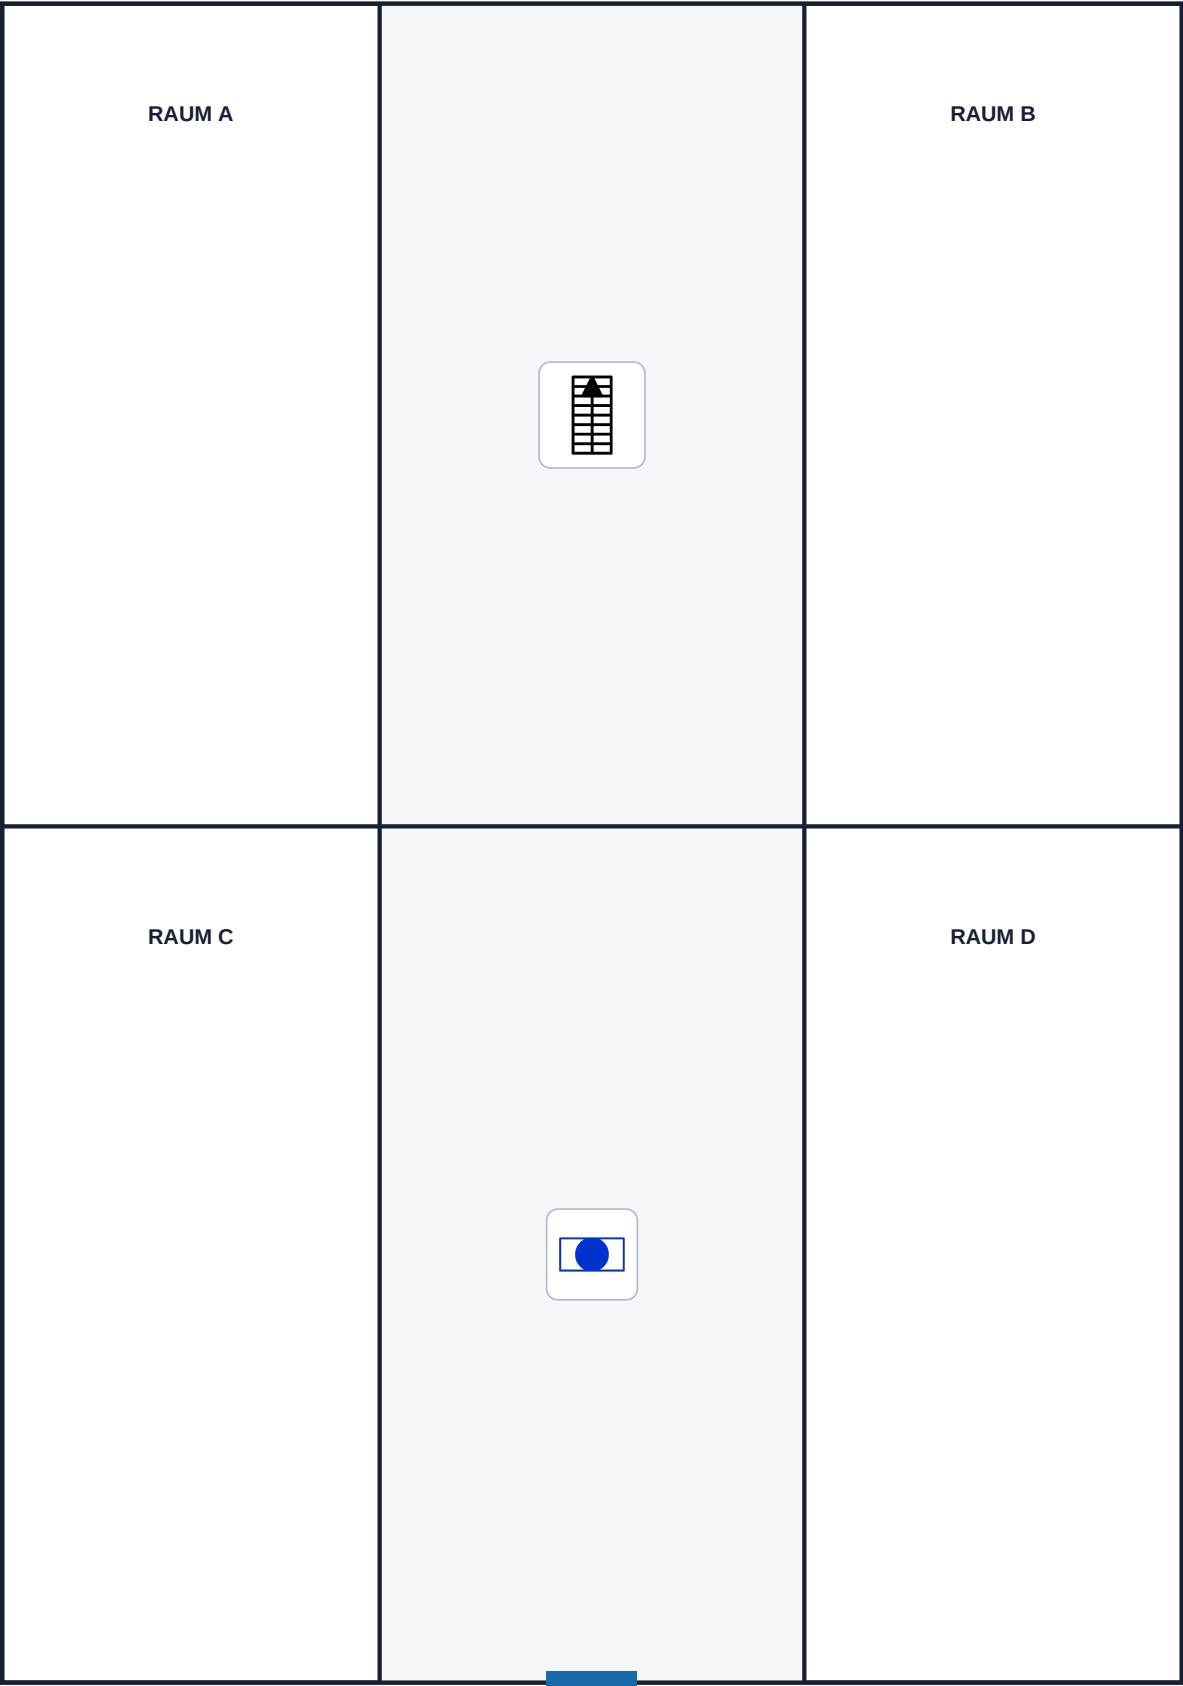

Schlossgasse 9, 4103 Bottmingen

DEMO - synthetisch, keine echten Objektdaten


ERDGESCHOSS

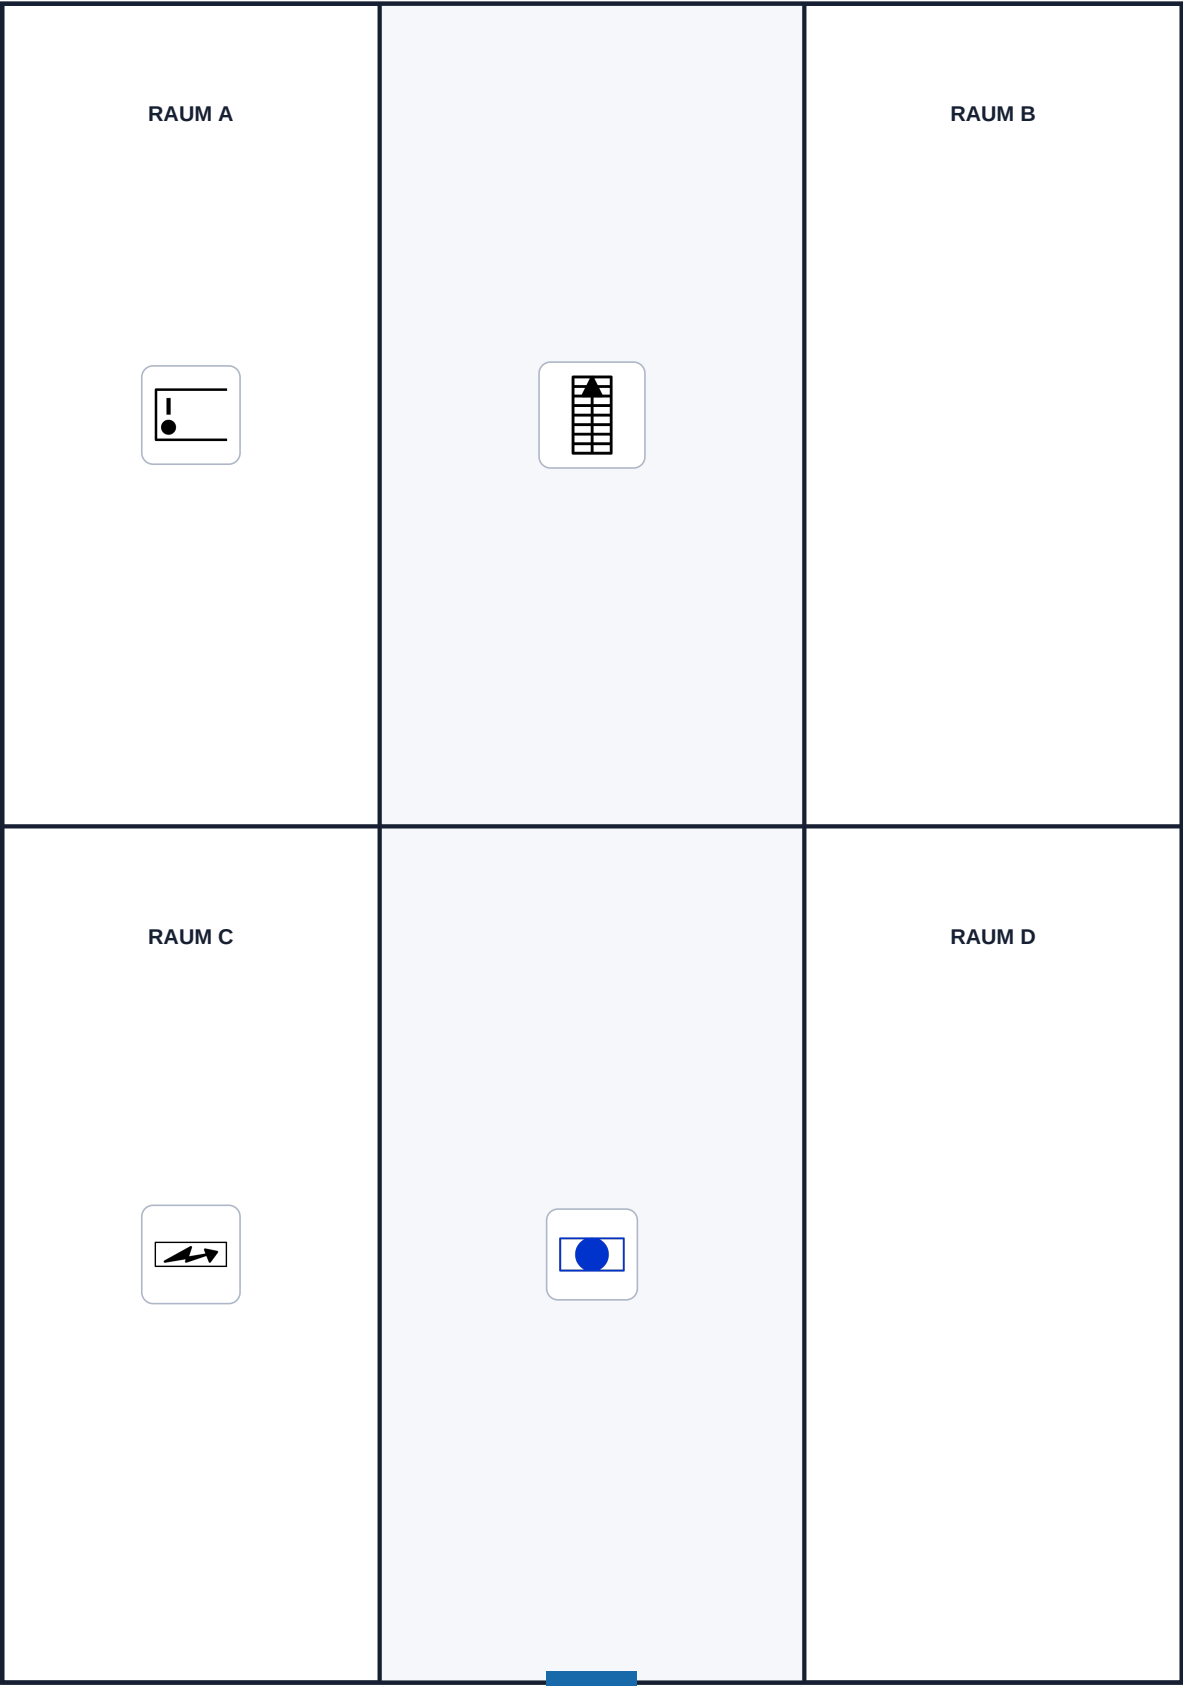

Schlossgasse 9, 4103 Bottmingen

DEMO - synthetisch, keine echten Objektdaten


1. OBERGESCHOSS

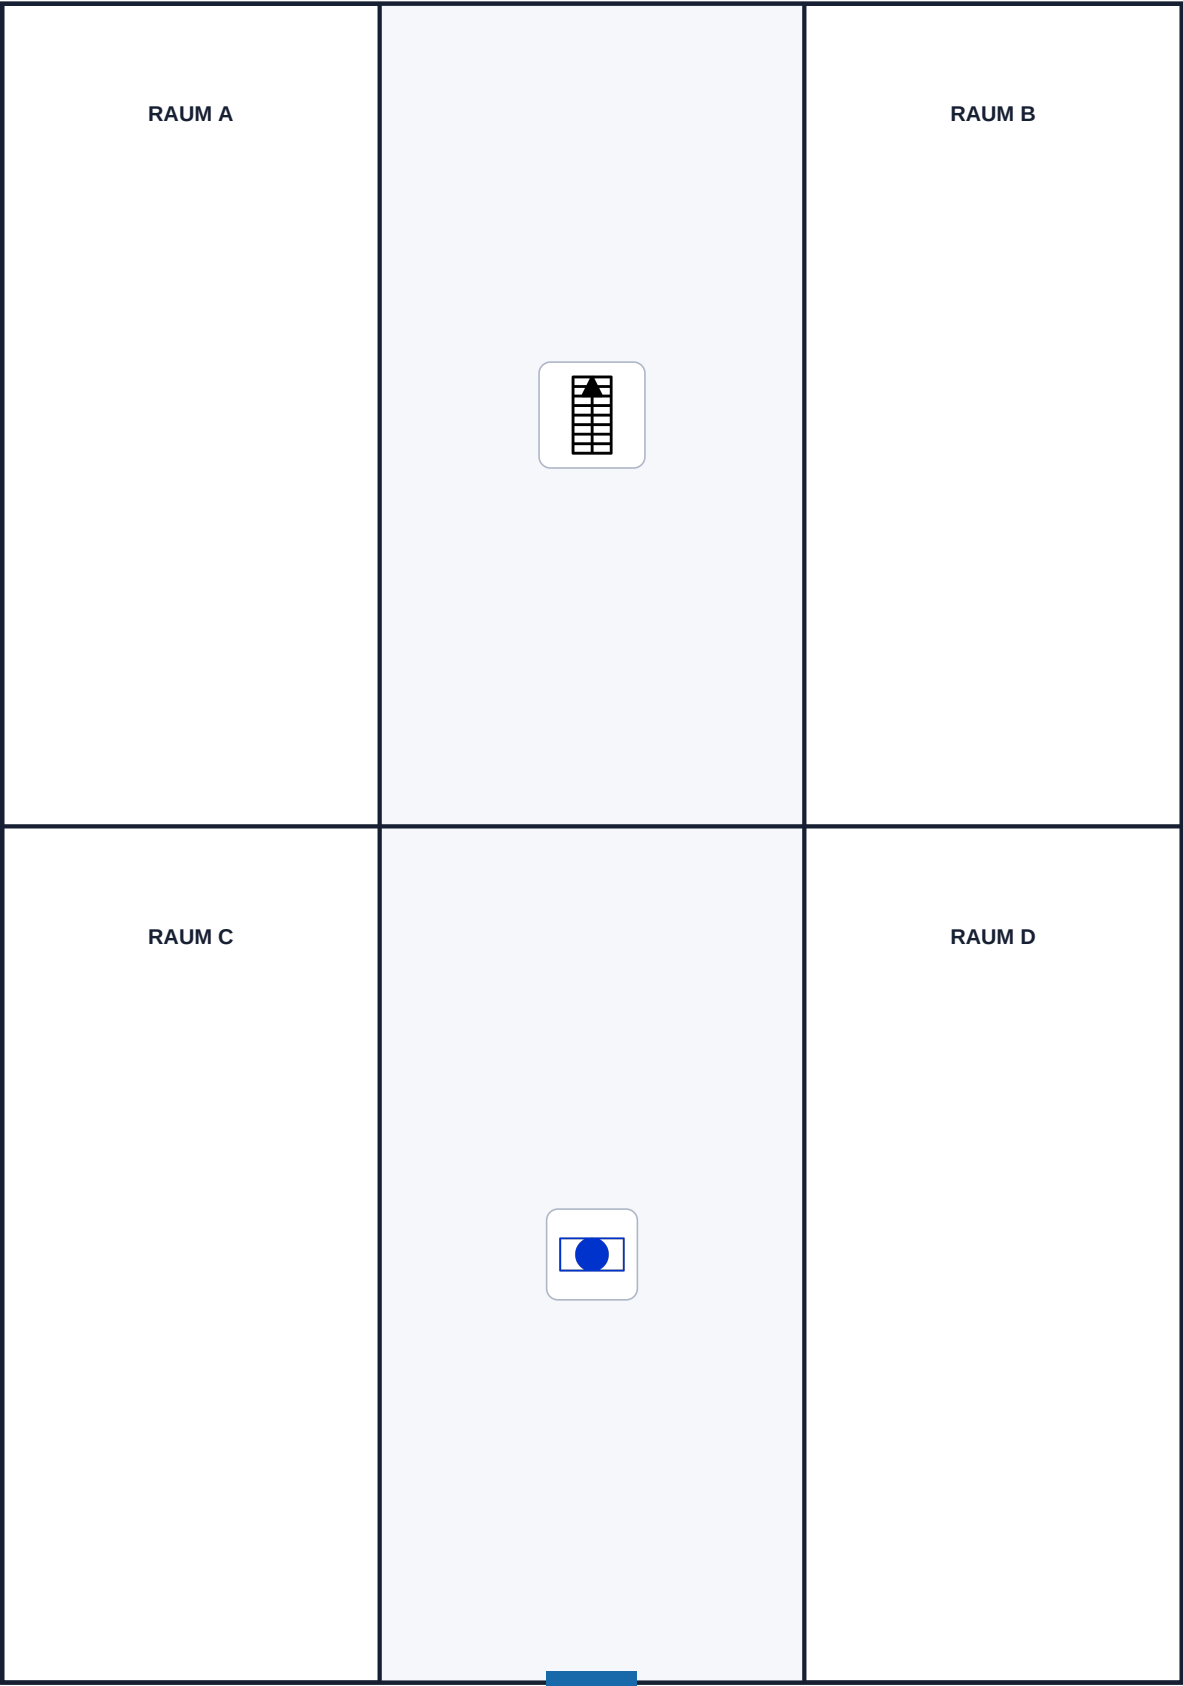

Schlossgasse 9, 4103 Bottmingen

DEMO - synthetisch, keine echten Objektdaten

2. OBERGESCHOSS

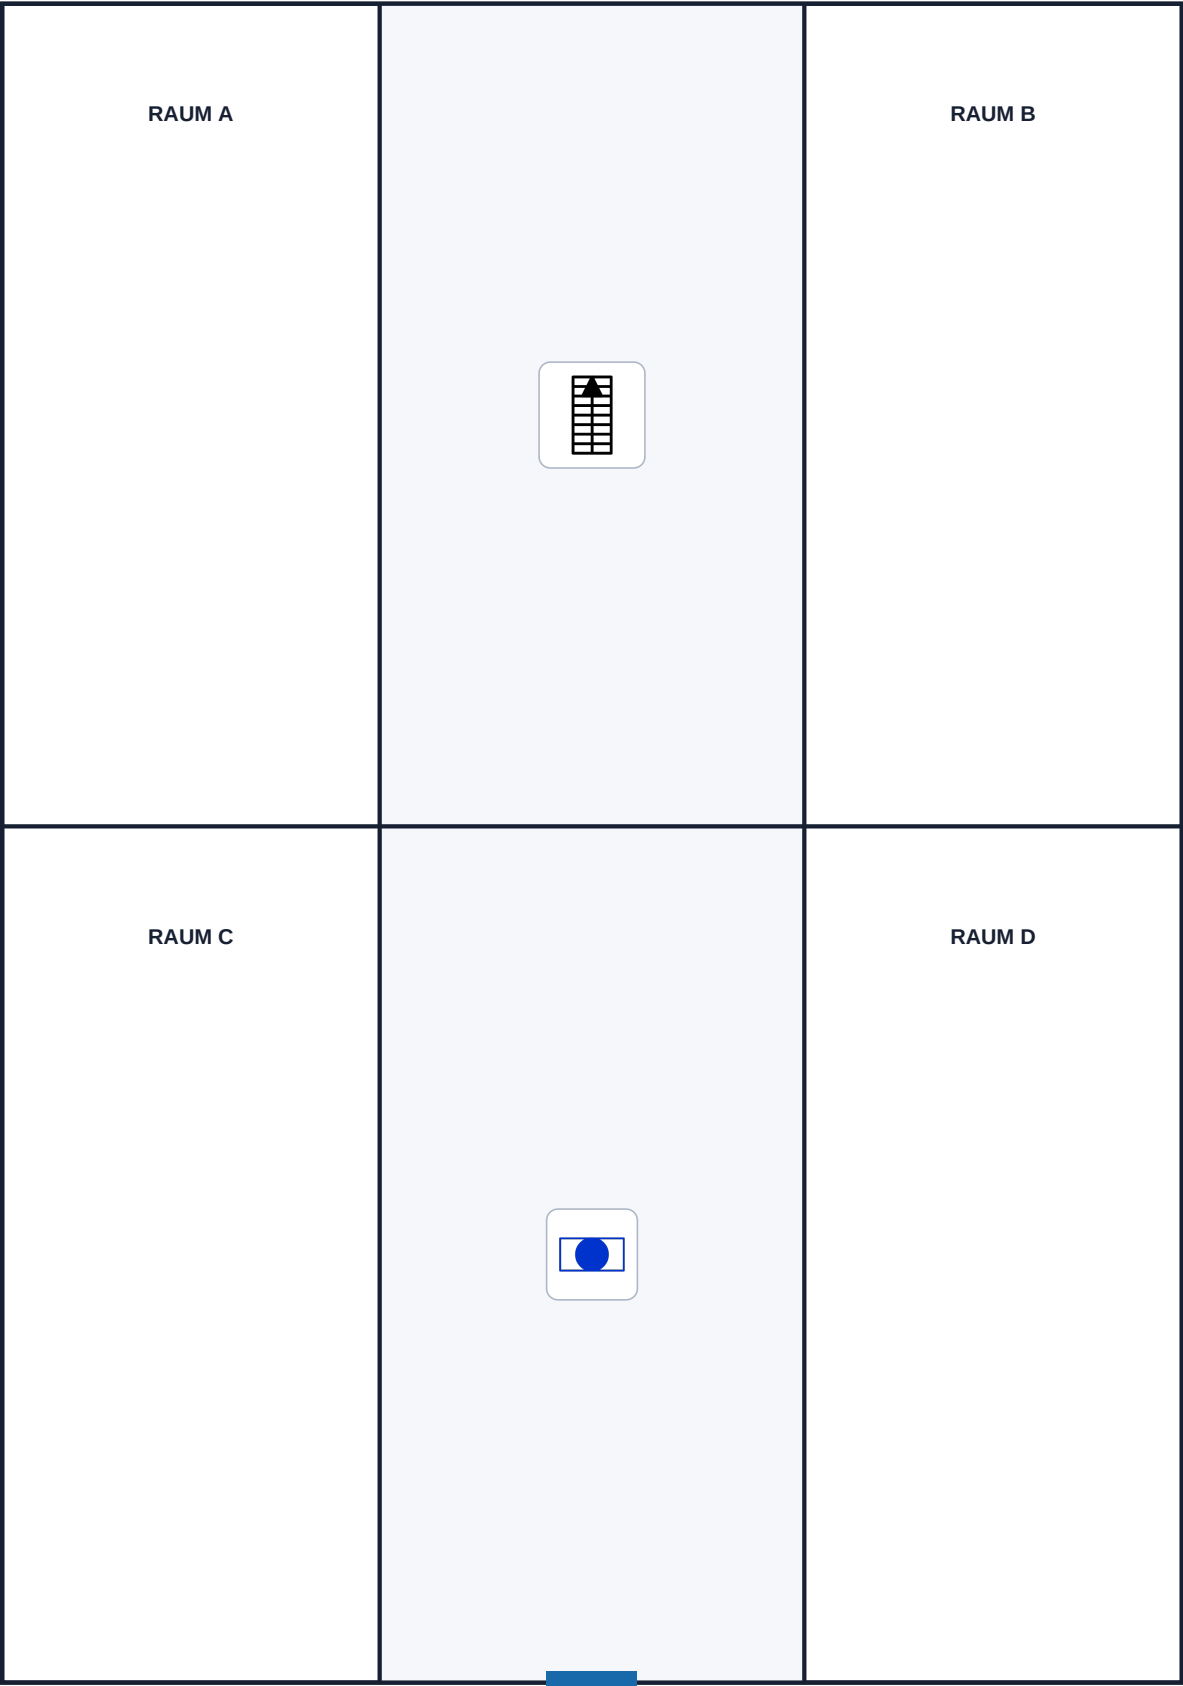

Schlossgasse 9, 4103 Bottmingen

DEMO - synthetisch, keine echten Objektdaten

3. OBERGESCHOSS

